더 아리랑 3층 22실 49인 생활공간 구획안

실 수·정원은 확정 요구 / 벽·창·출입구·기둥 좌표와 축척은 미확정 / 시공·인허가 도면 아님

좌측 생활구역 11실 · 24명

- 301호 1인실 — 침실 목표 12 m2 — 개별 WC 5.5 m2
- 302호 1인실 — 침실 목표 12 m2 — 개별 WC 5.5 m2
- 303호 1인실 — 침실 목표 12 m2 — 개별 WC 5.5 m2
- 304호 1인실 — 침실 목표 12 m2 — 개별 WC 5.5 m2
- 308호 2인실 — 침실 목표 20 m2 — 개별 WC 5.5 m2
- 309호 2인실 — 침실 목표 20 m2 — 개별 WC 5.5 m2
- 310호 2인실 — 침실 목표 20 m2 — 개별 WC 5.5 m2
- 315호 3인실 — 침실 목표 28 m2 — 개별 WC 5.5 m2
- 316호 3인실 — 침실 목표 28 m2 — 개별 WC 5.5 m2
- 319호 4인실 — 침실 목표 36 m2 — 개별 WC 5.5 m2
- 320호 4인실 — 침실 목표 36 m2 — 개별 WC 5.5 m2

중앙 공동 거실·식당

식당·거실 50 m2 / 조리실 49.59 m2 별도

개인 생활과 식사·교류를 연결 / 동시 급식인원 검토

중앙 동선 폭 목표 2.4m / 법정·실측 검토 전

조리실 15평

49.59 m2 / 반입·

프로그램실

40 m2 / 별도 활동실

물리·작업치료실

25 m2 / 기능 유지

의료·간호사실

18 m2 / 약품·기록

요양보호사실

18 m2 / 인계·업무

사무·상담실

20 m2 / 사회복지사

남 목욕·탈의

18 m2 / 보조 목욕

여 목욕·탈의

18 m2 / 보조 목욕

자원봉사자실

10 m2 / 별도 구획

직원 휴게실

16 m2 / 업무실과 분리

직원 탈의·사물함

16 m2 / 이용 분리

생활·위생 지원

세탁·청결·오염 분리

피난·대피 연결 검토 영역

계단 2개소·대피시설 위치는 원도면 및 현장 확인 후 결정

우측 생활구역 11실 · 25명

- 305호 1인실 — 침실 목표 12 m2 — 개별 WC 5.5 m2
- 306호 1인실 — 침실 목표 12 m2 — 개별 WC 5.5 m2
- 307호 1인실 — 침실 목표 12 m2 — 개별 WC 5.5 m2
- 311호 2인실 — 침실 목표 20 m2 — 개별 WC 5.5 m2
- 312호 2인실 — 침실 목표 20 m2 — 개별 WC 5.5 m2
- 313호 2인실 — 침실 목표 20 m2 — 개별 WC 5.5 m2
- 314호 2인실 — 침실 목표 20 m2 — 개별 WC 5.5 m2
- 317호 3인실 — 침실 목표 28 m2 — 개별 WC 5.5 m2
- 318호 3인실 — 침실 목표 28 m2 — 개별 WC 5.5 m2
- 321호 4인실 — 침실 목표 36 m2 — 개별 WC 5.5 m2
- 322호 4인실 — 침실 목표 36 m2 — 개별 WC 5.5 m2

침실 22실 모두 외기와 접한 개폐 창 검토 / 다인실 남녀 구분 / 1인실 중 특별침실 2실 배정 검토

모든 WC 면적은 침실 목표·법정 침실 면적과 분리 / 5.5 m2는 설계 예산이며 접근성 충족 판정이 아님

예산 면적 1,267.59 m2 / 기존 표기 400평 약 1,322.31 m2는 실측 및 인정 면적 확인 전

중앙 복도 2.4m·생활 복도 1.8m는 설계 목표 / 실제 피난·편의시설 기준과 침상 회전 검증 필요


공간 관계를 구분한 설계 브리프입니다. 이 도형의 폭·길이를 실제 실 치수로 사용하지 마십시오.

더 아리랑 | 4층 인테리어 기본계획

어르신 쉼터 · 활동과 휴식

견적·협의용 v1 / 시공용·인허가 도면 아님 / 기존 구조 그리드 참고 / 실측 후 확정 / 2026.10.06

기준 그리드 39,200 mm

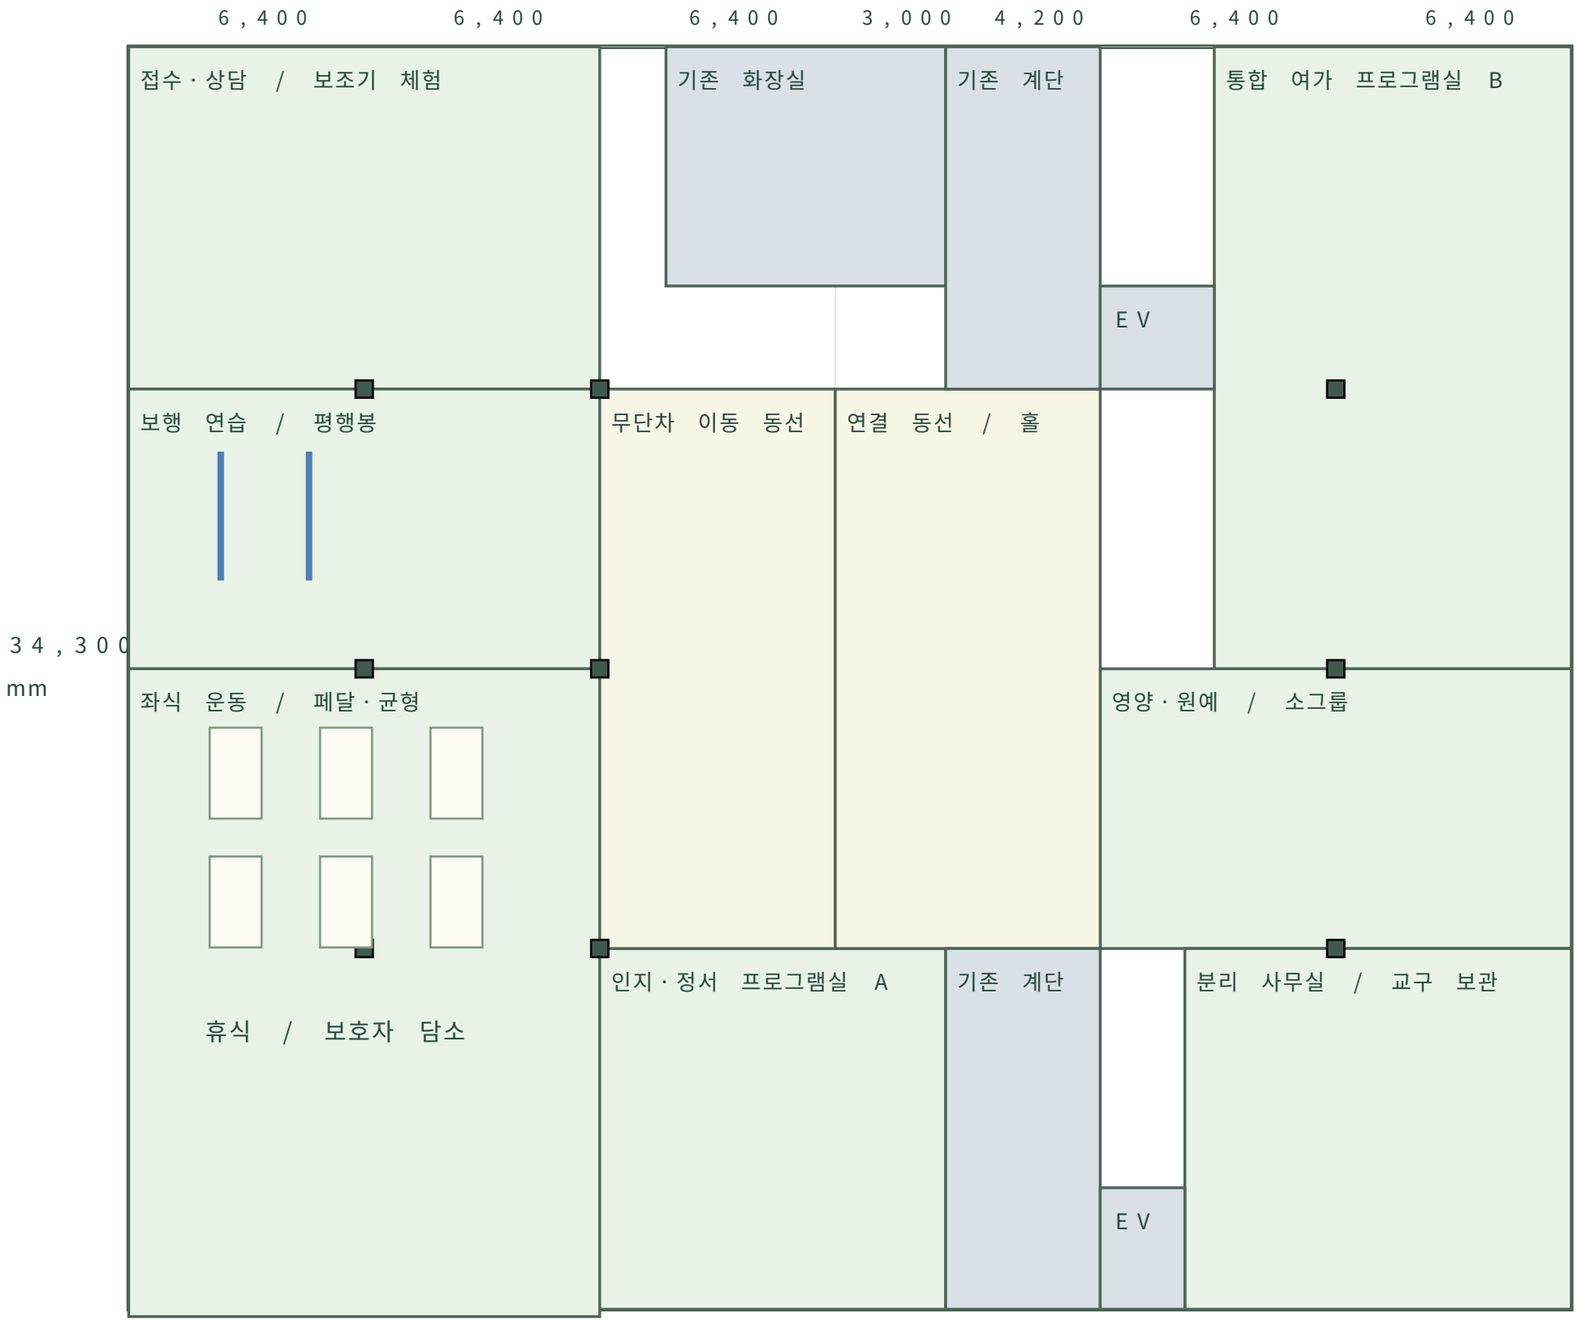

설계·견적 확인 사항

외곽·계단·승강기·기둥은 기존 도면 참고.

벽·구획·문 위치 및 치수는 현장 실측 후 확정.

표기 치수는 구조 그리드(mm).

그리드 면적은 건축물대장 면적과 다름.

기존 용도변경 승인을 뜻하는 도면이 아님.

피난·방화구획·소방·배연은 전문 설계 검토.

무단차·회전 공간·접근 가능한 화장실 검토.

조명·전기·급배수·공조는 실시설계 반영.

가구·기기 수량과 의료 장비는 별도 협의.

원본 PDF·원본 이미지가 없는 재작성본.

복지지원·바우처 종목은 지자체 확인 필요.

사업별 자격 인력·독립실·등록 요건 검토.

A·B실은 독립실 제안. 실제 면적 확정 필요.

운동·인지·원예·영양 중심의 체험 구상.


치료·안마는 별도 자격·개설 요건 확인.

더 아리랑 | 5층 인테리어 기본계획

옥상 · 중앙 휴식과 좌우 정원

견적·협의용 v1 / 시공용·인허가 도면 아님 / 기존 구조 그리드 참고 / 실측 후 확정 / 2026.10.06

기준 그리드 39,200 mm

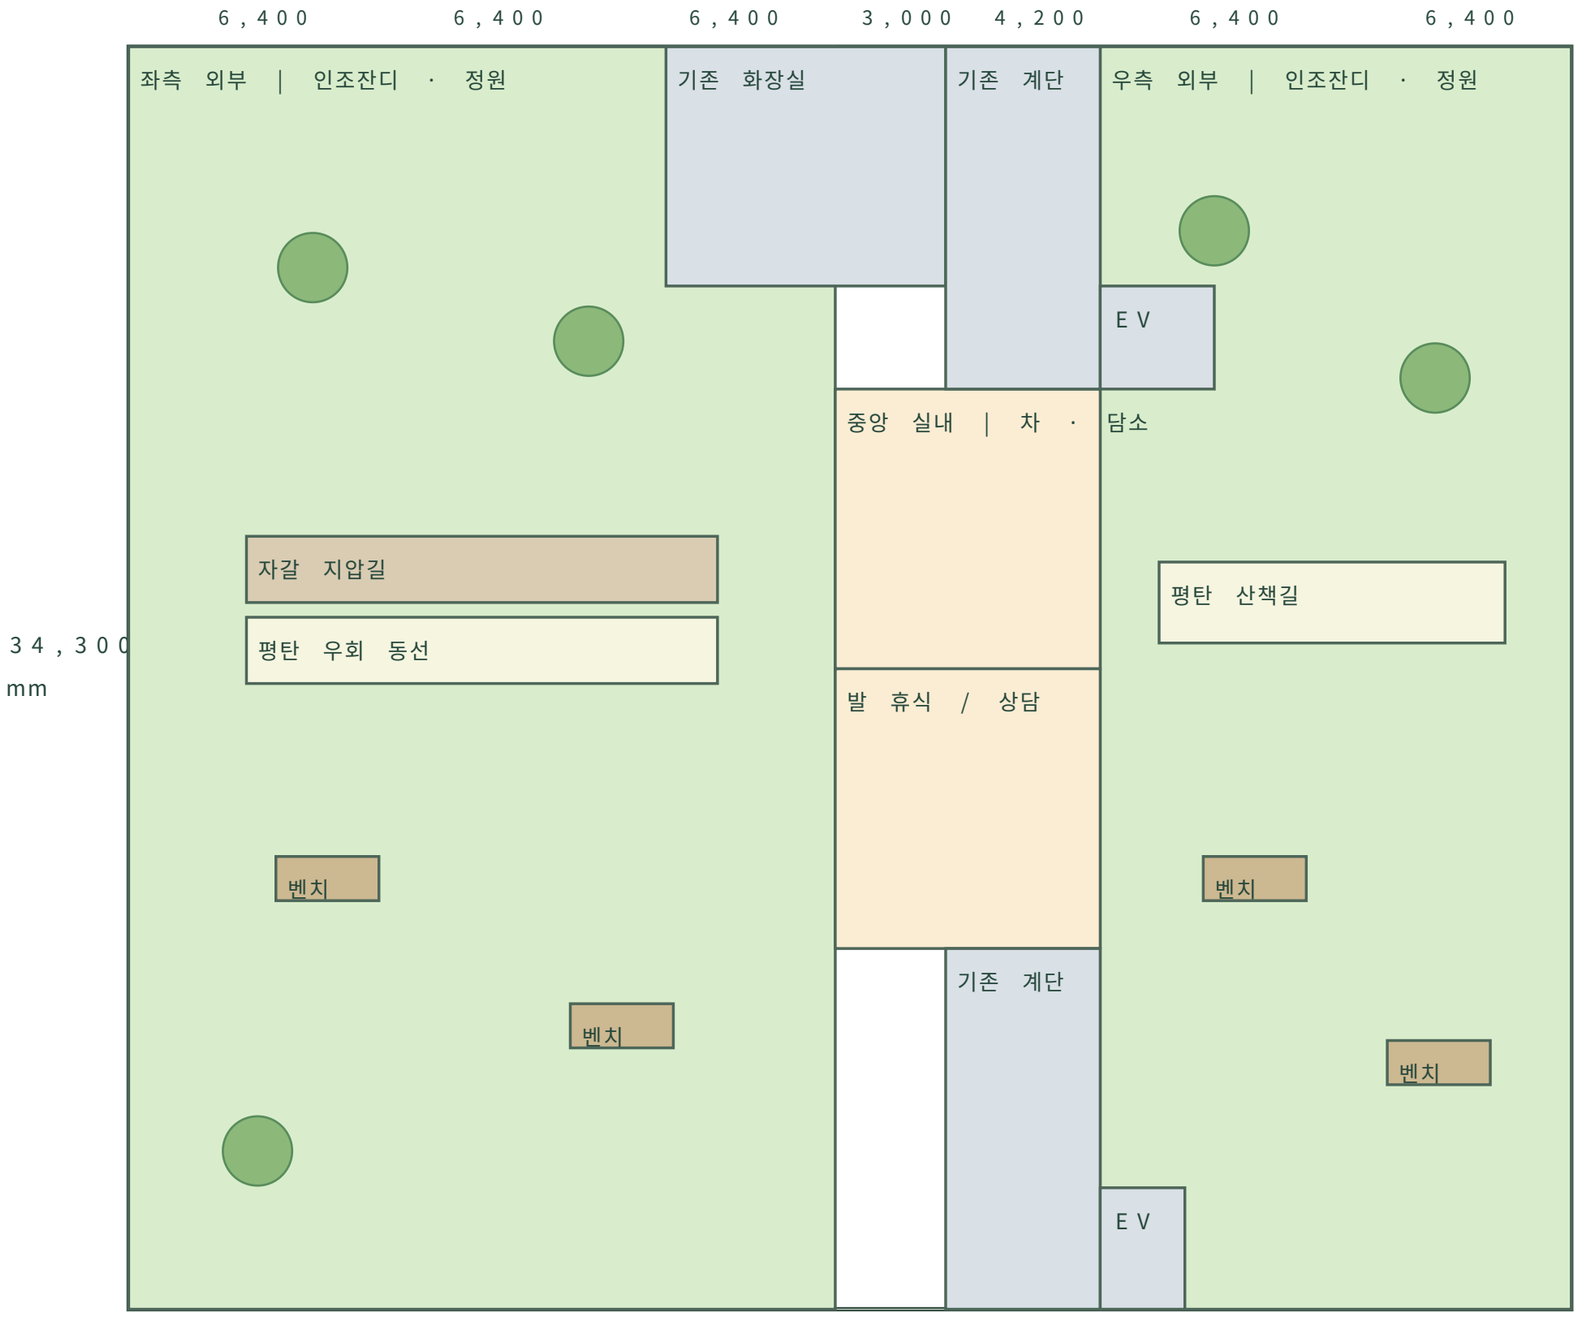

설계·견적 확인 사항

외곽·계단·승강기·기둥은 기존 도면 참고.

벽·구획·문 위치 및 치수는 현장 실측 후 확정.

표기 치수는 구조 그리드(mm).

그리드 면적은 건축물대장 면적과 다름.

기존 용도변경 승인을 뜻하는 도면이 아님.

피난·방화구획·소방·배연은 전문 설계 검토.

무단차·회전 공간·접근 가능한 화장실 검토.

조명·전기·급배수·공조는 실시설계 반영.

가구·기기 수량과 의료 장비는 별도 협의.

원본 PDF·원본 이미지가 없는 재작성본.

중앙 실내와 좌우 외부를 구분한 정원 구상.

기존 도면의 5층 실내 면적 266.09㎡ 참고.

옥상 하중·방수·배수·난간·풍압 검토 필수.

자갈길 옆에 평탄한 우회 동선 확보.

초음파 치료는 의료인·법적 조건 검토 후.

지붕·유리 구획 현 상태는 현장 확인 필요.